



CI 19 - 03

App 2

ÉCHELLE D'UN DOCUMENT

Nom:

Date: / /

01/03

Classe:

Gr:

CAS 1 : PLAN DE R.D.C.

Q1 - Calculer à partir de l'échelle LES 4 DIMENSIONS RÉELLES (EN MÈTRE) du plan ci-dessous :

/ 8

Q2 - Donner les DIMENSIONS RÉELLES de la chambre 2 : LONGUEUR = **4,32 m** / LARGEUR = **3,13 m**



CI 19 - 03

App 2

ÉCHELLE D'UN DOCUMENT

Nom:

Date: / /

02/03


Classe:

Gr:

CAS 2 : ÉCHELLE GRADUÉE

Q3 - Retrouver à partir de l'échelle graduée LES 3 DIMENSIONS RÉELLES (EN MÈTRE) du plan ci-dessous :

/ 6

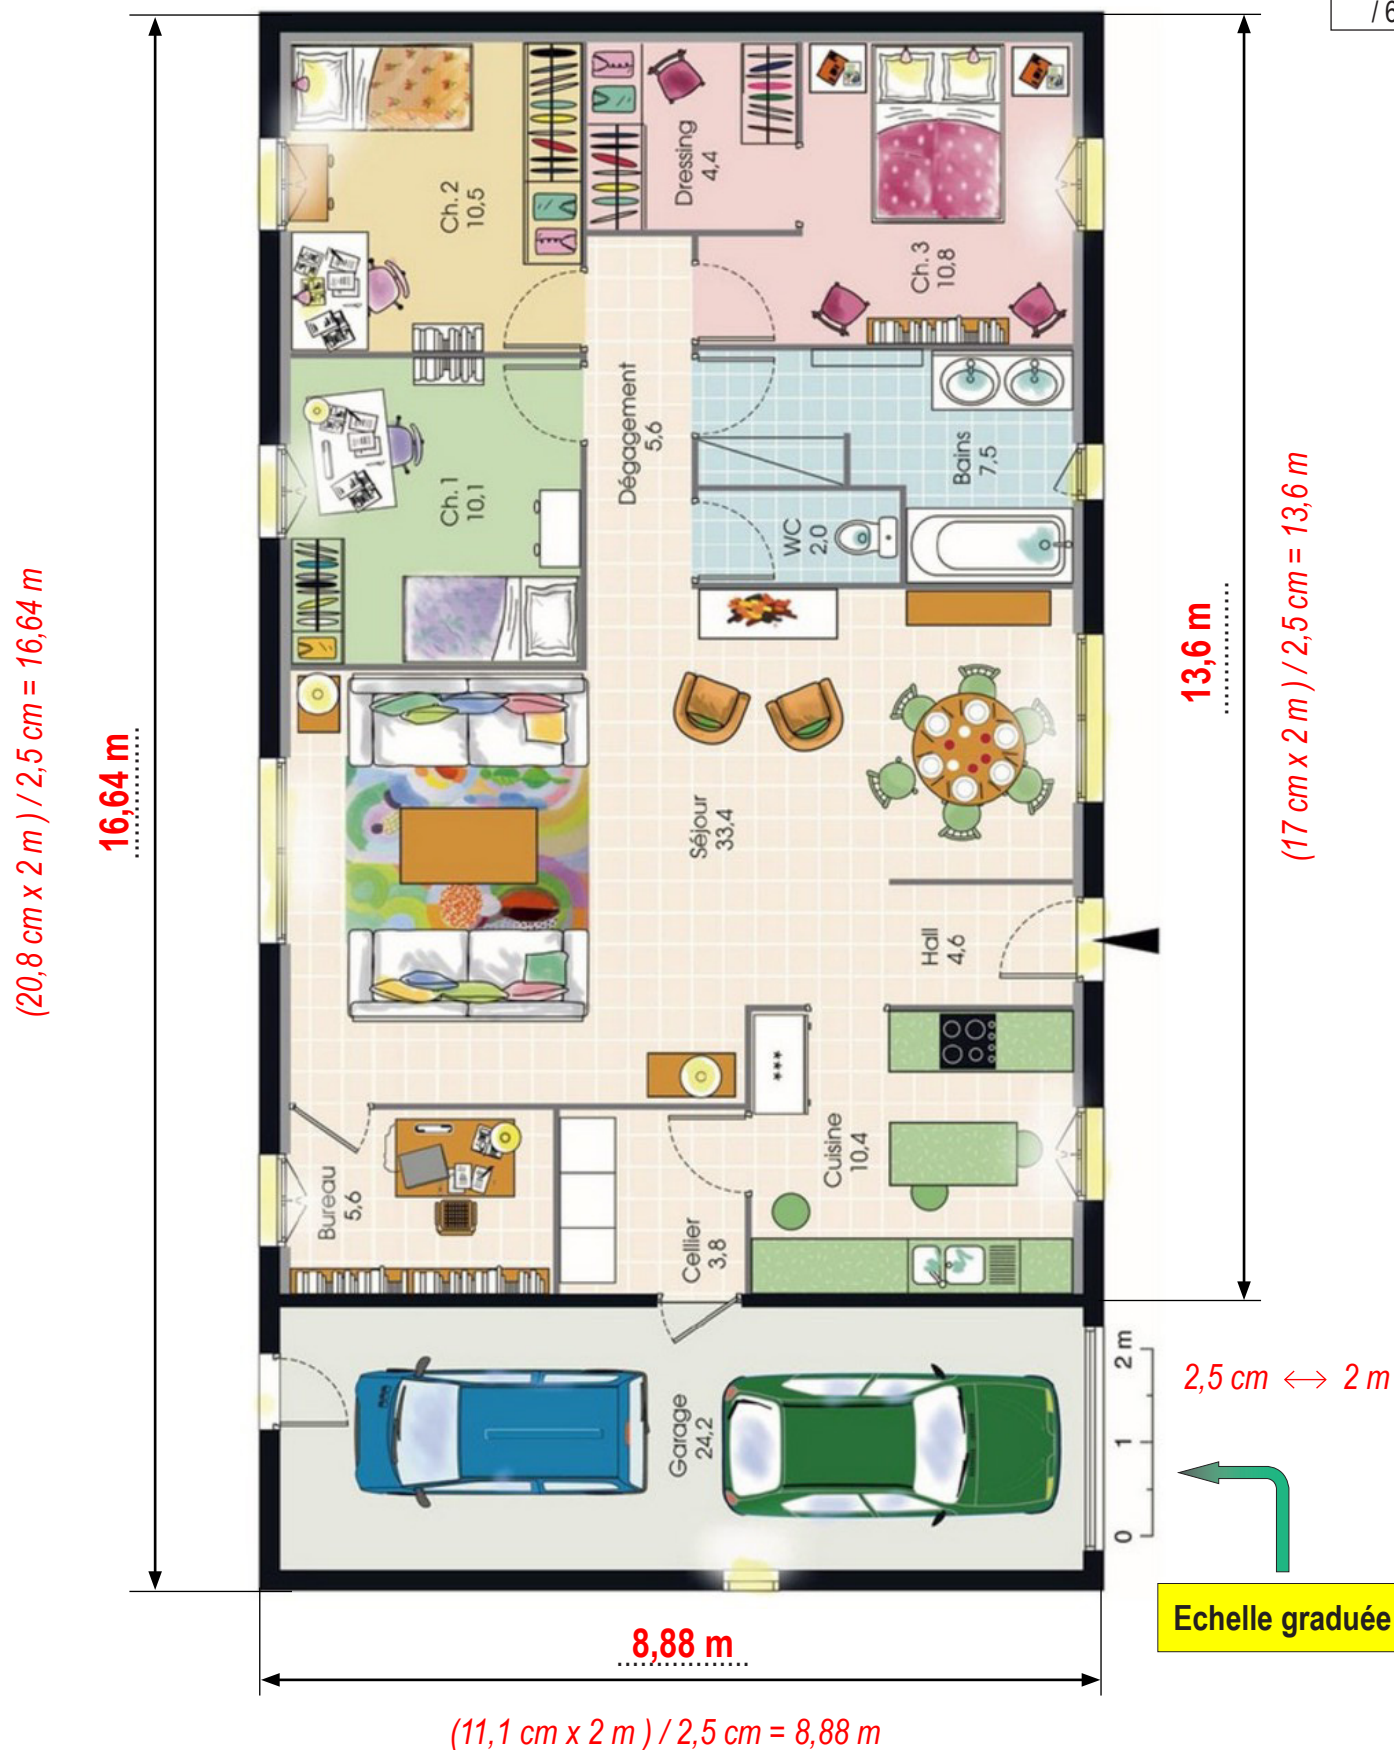



CI 19 - 03

App 2

Date: / /

03/03

ÉCHELLE D'UN DOCUMENT

Nom:

Classe:


Gr:

CAS 3 : PLAN DE FAÇADES

Q4 - Calculer L'ÉCHELLE des plans de façades ci-dessous (à partir de la dimension 14,85 m) :

/ 3

FAÇADE PRINCIPALE

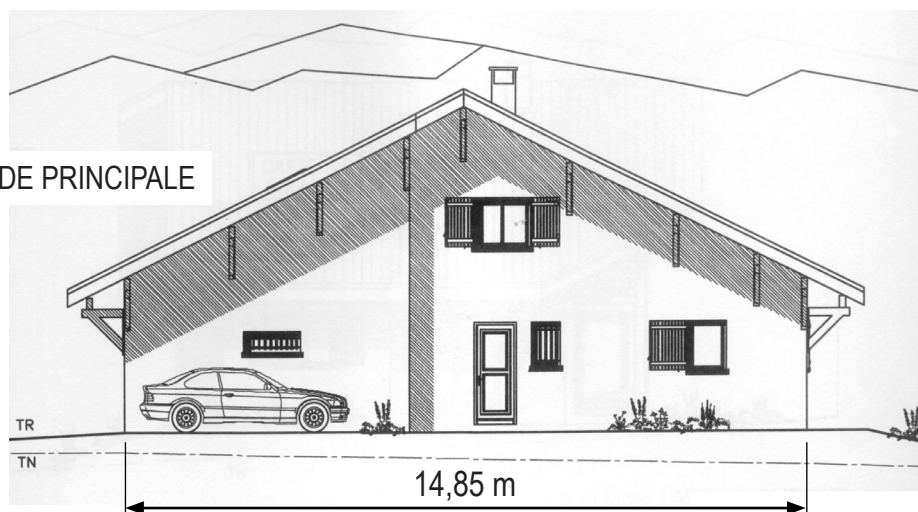

Calcul :

$$\text{échelle} = \frac{\text{Dimension réelle}}{\text{Dimension mesurée}}$$

$$\text{échelle} = \frac{1485 \text{ (cm)}}{8,7 \text{ (cm)}}$$


$$\text{échelle} = 1:170$$

Echelle: **1 : 170**

Q5 - En déduire la HAUTEUR de la maison sur l'image ci-dessous (échelle identique) :

/ 1

FAÇADE ARRIÈRE

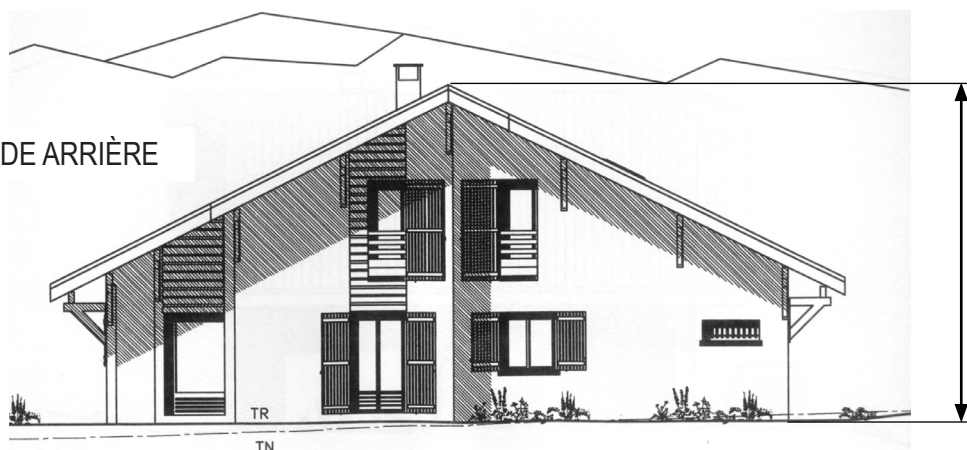


Calcul :

$$4,5 \times 170 = 765 \text{ cm} \\ = 7,65 \text{ m}$$

Q6 - En déduire la LARGEUR de la maison sur l'image ci-dessous (échelle identique) :

/ 1

FAÇADE GAUCHE

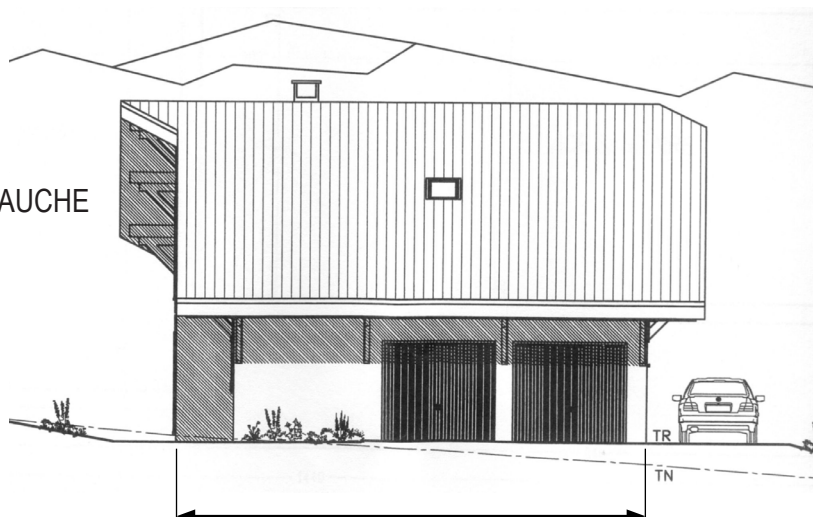

Calcul :

$$6,2 \times 170 = 1054 \text{ cm} \\ = 10,54 \text{ m}$$